
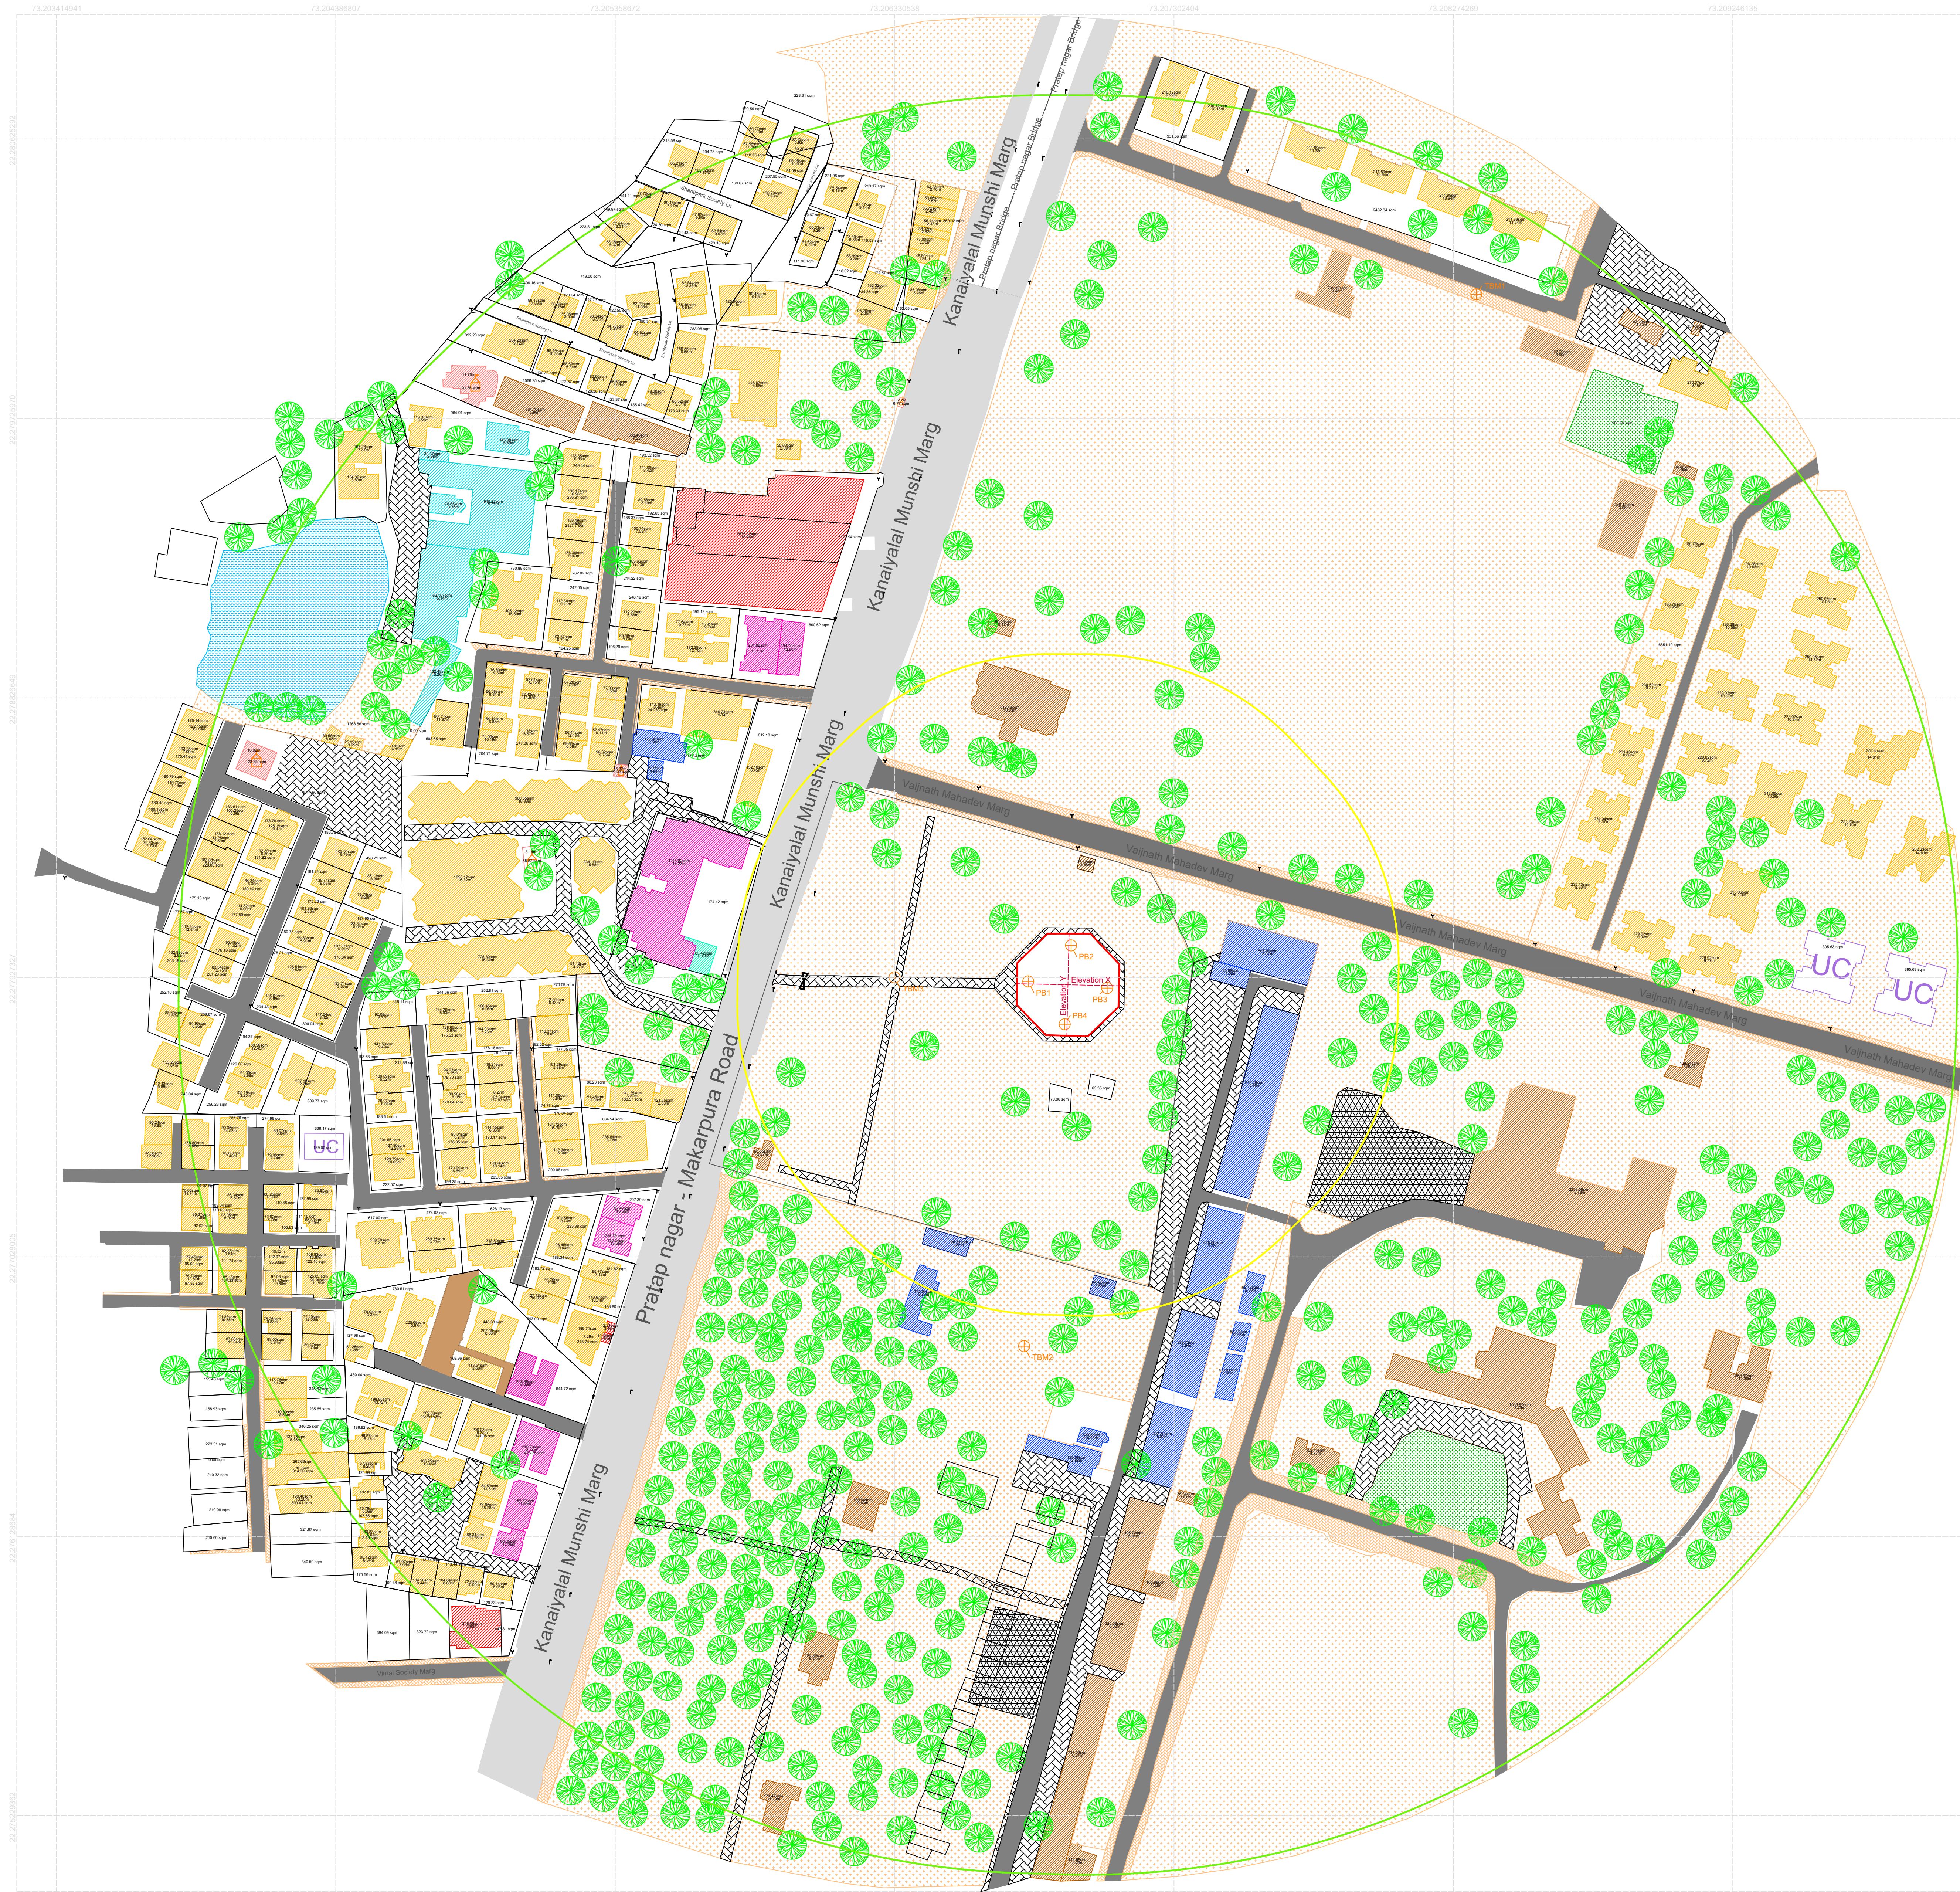


SITE PLAN SHOWING THE PROTECTED, PROHIBITED AND REGULATED BOUNDARY OF HAZIA AT DANTESHWAR VILLAGE, TALUKA- BARODA, (NOW KNOWN AS HAZIRA OR QUTBUDDIN MAHMAD KHAN'S TOMB AT DANTESHWAR, VADODARA CITY, TALUKA-VADODARA), DISTRICT- VADODARA, GUJARAT

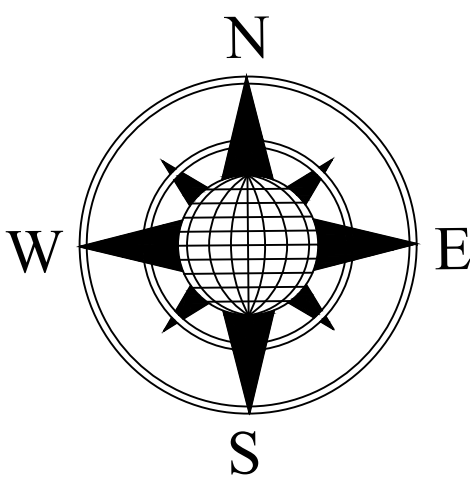

LEGEND

Hazira - Mapping Area Height 01

DESCRIPTION	SYMBOL	DESCRIPTION	SYMBOL
PROTECTED BOUNDARY		TREE	
PROHIBITED BOUNDARY		STREET LIGHT	
REGULATED BOUNDARY		ELECTRIC POLE	
BUILDING - RESIDENTIAL		FOOTPATH	
BUILDING - COMMERCIAL		BENCHMARK POINTS	
BUILDING - EDUCATIONAL		ASI - Fence Boundary	
BUILDING - PUBLIC / SEMI PUBLIC		WATER BODY	
BUILDING (MIXED USE) - COMMERCIAL & RESIDENTIAL		FLYOVER	
BUILDING - RELIGIOUS		GATE OF THE MONUMENT	
GREEN SPACES		EARTHEN ROAD	
HEALTH SERVICES		CEMETERY	
OPEN LAND		UNDER CONSTRUCTION	
PAVED AREA		PARKING	
PLOT BOUNDARY			
ROADS- PRIMARY			
ROADS- SECONDARY			
ROADS- TERTIARY			


SITE PHOTOGRAPHS



ELEVATION X



ELEVATION Y

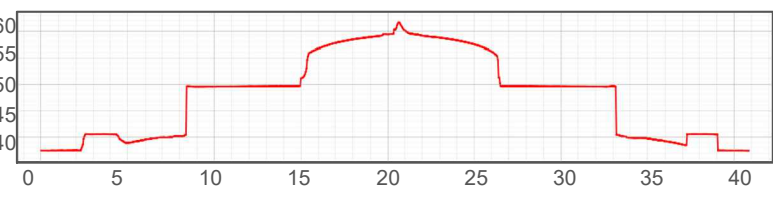

AREA STATEMENT

AREA OF LAND UNDER PROTECTED BOUNDARY (A) = 1104.18 SQM / 0.272848 ACRE
AREA OF LAND UNDER PROHIBITED BOUNDARY (B) = 43514.07 SQM / 10.7525 ACRE
AREA OF LAND UNDER REGULATED BOUNDARY (C) = 275523.71 SQM / 68.0834 ACRE
TOTAL AREA = A + B + C = 320141.96 SQM / 79.1088 ACRE

SITE COORDINATES

Sr. no.	LATITUDE	LONGITUDE
PB1	22.277914260	73.206794742
PB2	22.278031210	73.206925140
PB3	22.277893422	73.207068557
PB4	22.277776210	73.206921128

TBM DETAILS

Sr. no.	EASTING	NORTHING	ELEVATION
TBM1	1188865.49908E	990309.47055N	54 M
TBM2	1188708.3015E	989931.4538N	58 M
TBM3	1188660.3914E	990062.7016N	53 M

OTHER DETAILS

- HEIGHT OF THE MONUMENT = 24.63 M
- ALL DIMENSIONS ARE IN METERS UNLESS OTHERWISE SPECIFIED
- CONTOUR INTERVAL = 0.5 M
- SURVEY DATE: 06/07/2026
- DRAWING NUMBER: 01
- UTM PROJECTION: EPSG: 7761 - WGS 84

SCALE

1:1000@A0



CLIENT



Archaeological Survey of India

(Vadodara Circle)
Puratattva Bhavan, Mandvi, Near Central Library,
Mandvi, Vadodara, Gujarat - 390006

SURVEY CONSULTANT



Ajnhawk Technologies Pvt. Ltd.

(Ahmedabad Office)
VS Fortune, 912, Addor Aspire 2, University
Road, Panjarapol, Ahmedabad - 380015



SURVEYOR

SUPERINTENDING ARCHEOLOGIST

REGIONAL DIRECTOR